



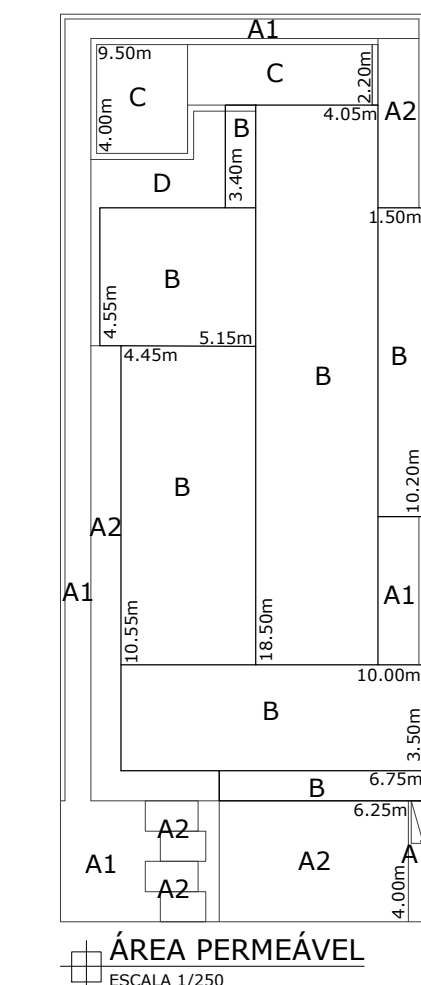


QUADRO DE ÁREA PERMEÁVEL		
A1	MATERIAL TIPO 1 (GRAMA)	46,67m²
A2	PISO DRENANTE ECO.	57,36m²
ÁREA DO TERRENO		360,00m²
ÁREA PERMEÁVEL		104,03m²
28,90% DA ÁREA DO TERRENO		

QUADRO DE ÁREA IMPERMEÁVEL		
B	EDIFICAÇÃO PRINCIPAL	205,76m²
C	PISCINA	27,43m²
D	DECK EM PORCELANATO	18,59m²
ÁREA DO TERRENO		360,00m²
ÁREA IMPERMEÁVEL		251,78m²
69,93% DA ÁREA DO TERRENO		

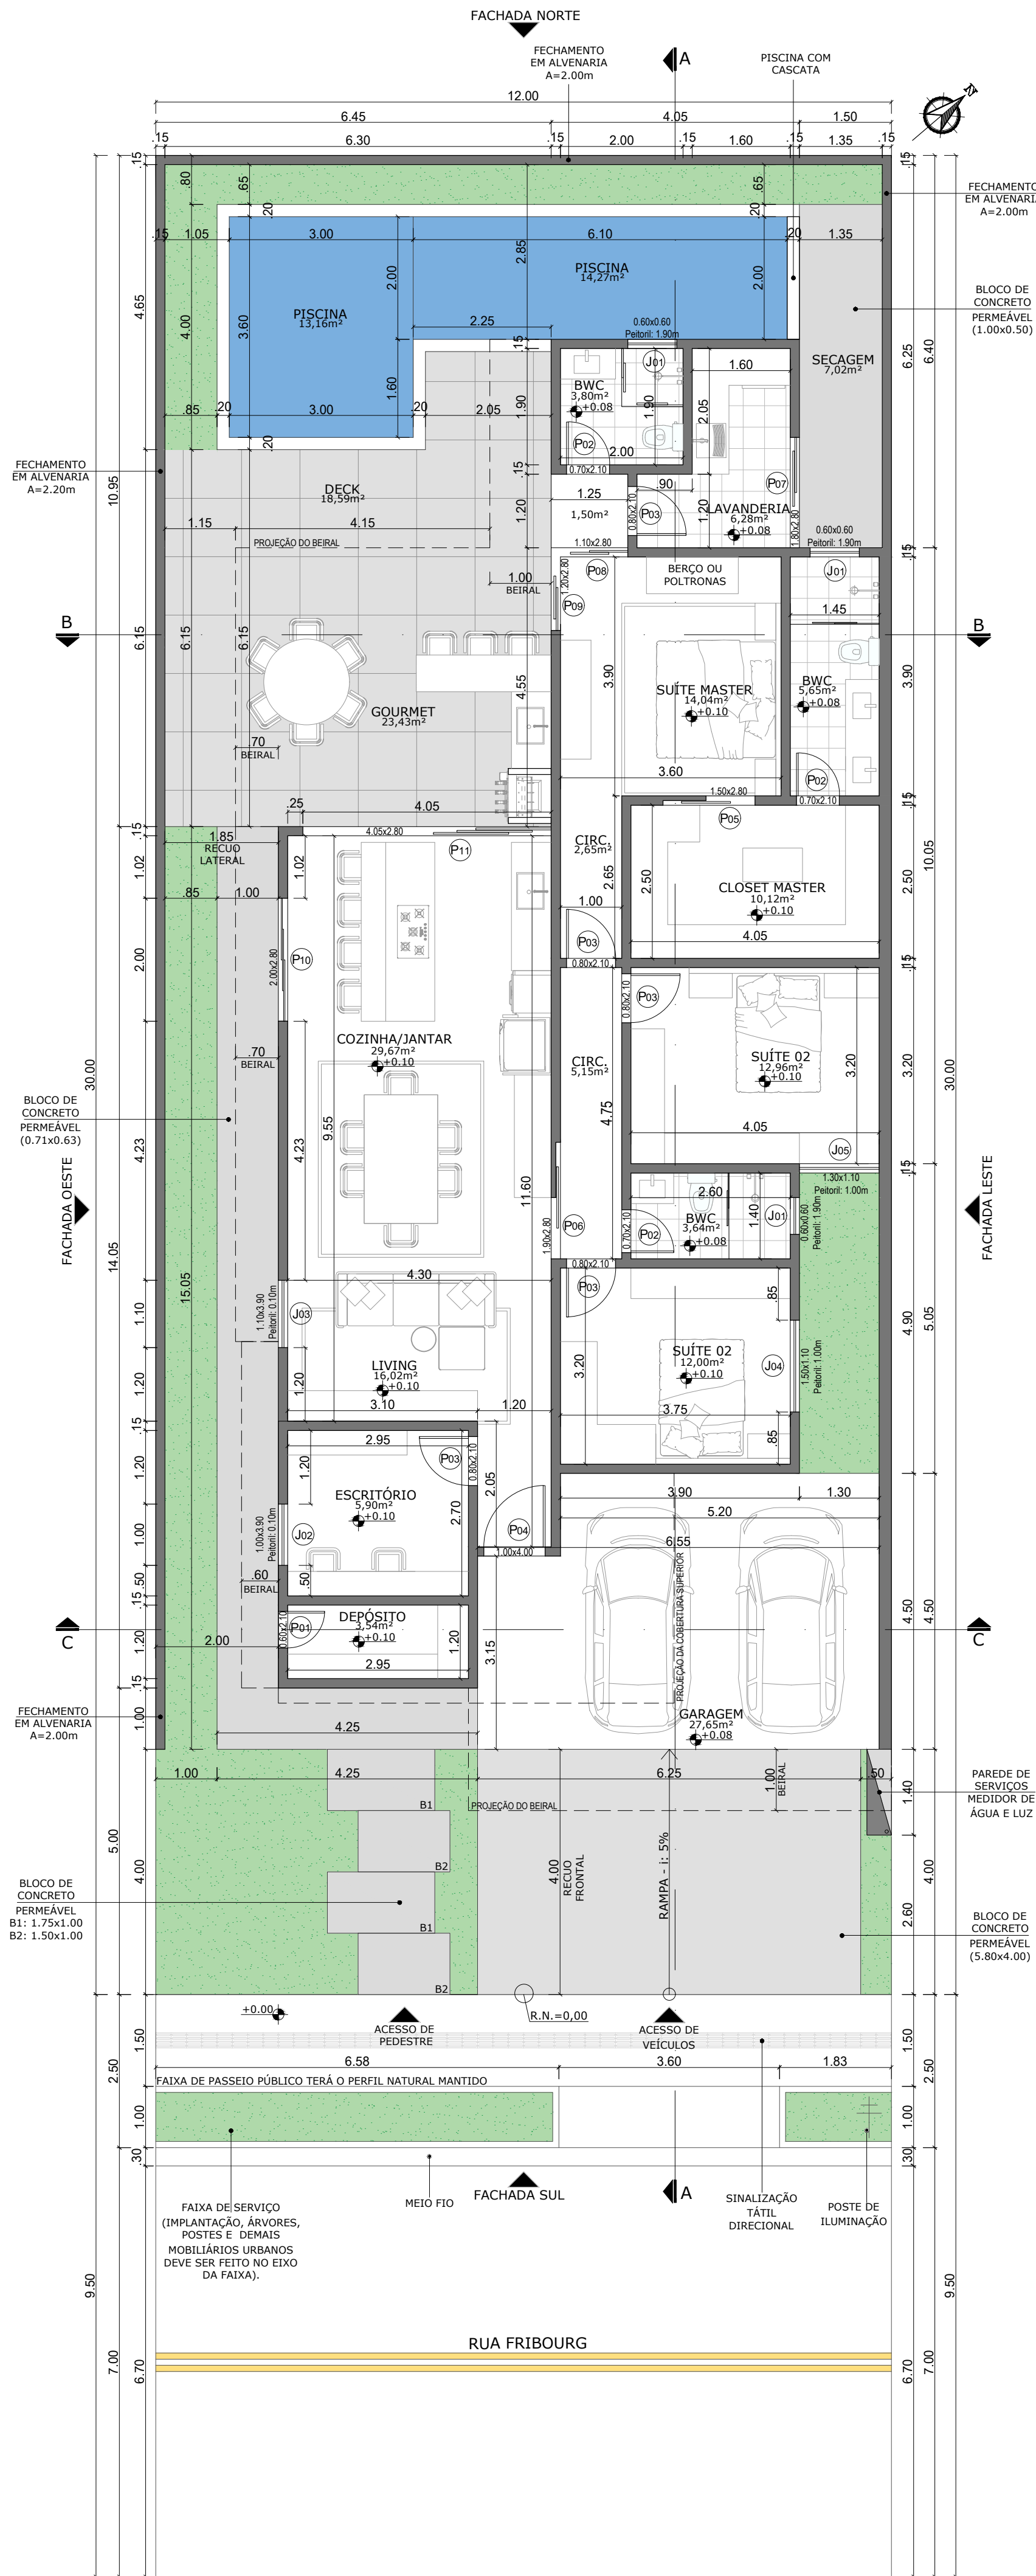

PLANTA DE SITUAÇÃO

ESCALA 1/1000

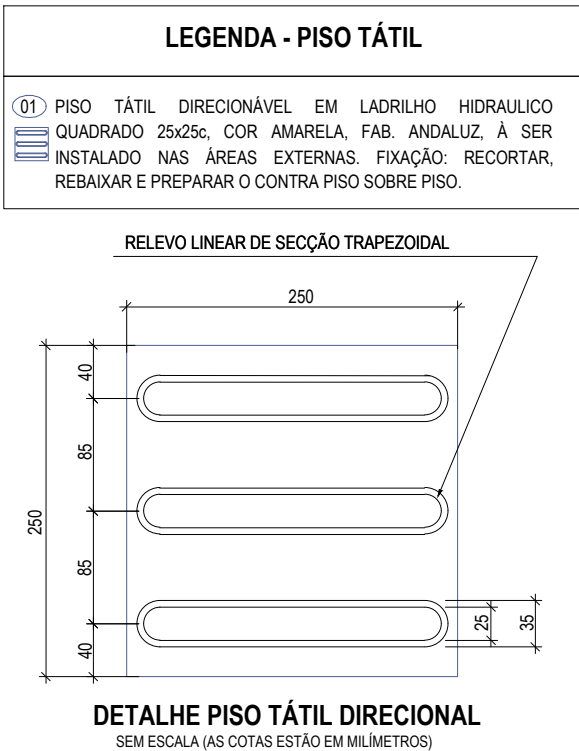

MARCOS DINIZ - ENGENHARIA

PROPRIETÁRIO:

ENGENHEIRO:

ASSINATURAS DIGITAL:

APROVAÇÃO CONDOMÍNIO:

APROVAÇÃO PREFEITURA:

ASSUNTO: PROJETO ARQUITETÔNICO

PROPRIETÁRIO: PATRICK DE FREITAS ALVES
CPF: 648.736.682-04

ENDEREÇO: ESTRADA DO CALAFATE, CONDOMÍNIO SWISS PARQUE
RUA FRIBOURG, QUADRA J, LOTE 26 - (RIO BRANCO - AC)

ENGENHEIRO: FRANCISCO MARCOS DINIZ FERNANDES
CREA - 0120271206

CONTEÚDO: MAPA DE SITUAÇÃO, PLANTA BAIXA TÉCNICA PAV. TÉRREO, QUADRO DE ESQUADRIAS, DETALHE DE PISO TÁTIL E QUADRO DE ÁREAS

ÁREAS: CONSTRUÍDA COBERTA: 205,76m²
PISCINA: 27,43m² | DECK: 18,59m²
ÁREA RESULTANTE: 233,18m²
TERRENO: 360,00m²

TAXAS: TAXA DE OCUPAÇÃO: 57,15%
COEFICIENTE DE APROVEITAMENTO: 0,57
TAXA DE PERMEABILIDADE: 28,90%
TAXA DE IMPERMEABILIDADE: 69,93%

PRANCHA:
01/04

ESCALA: INDICADA

DATA: JUNHO/2026

DESENHO TÉCNICO:
JULIANO BANDEIRA